
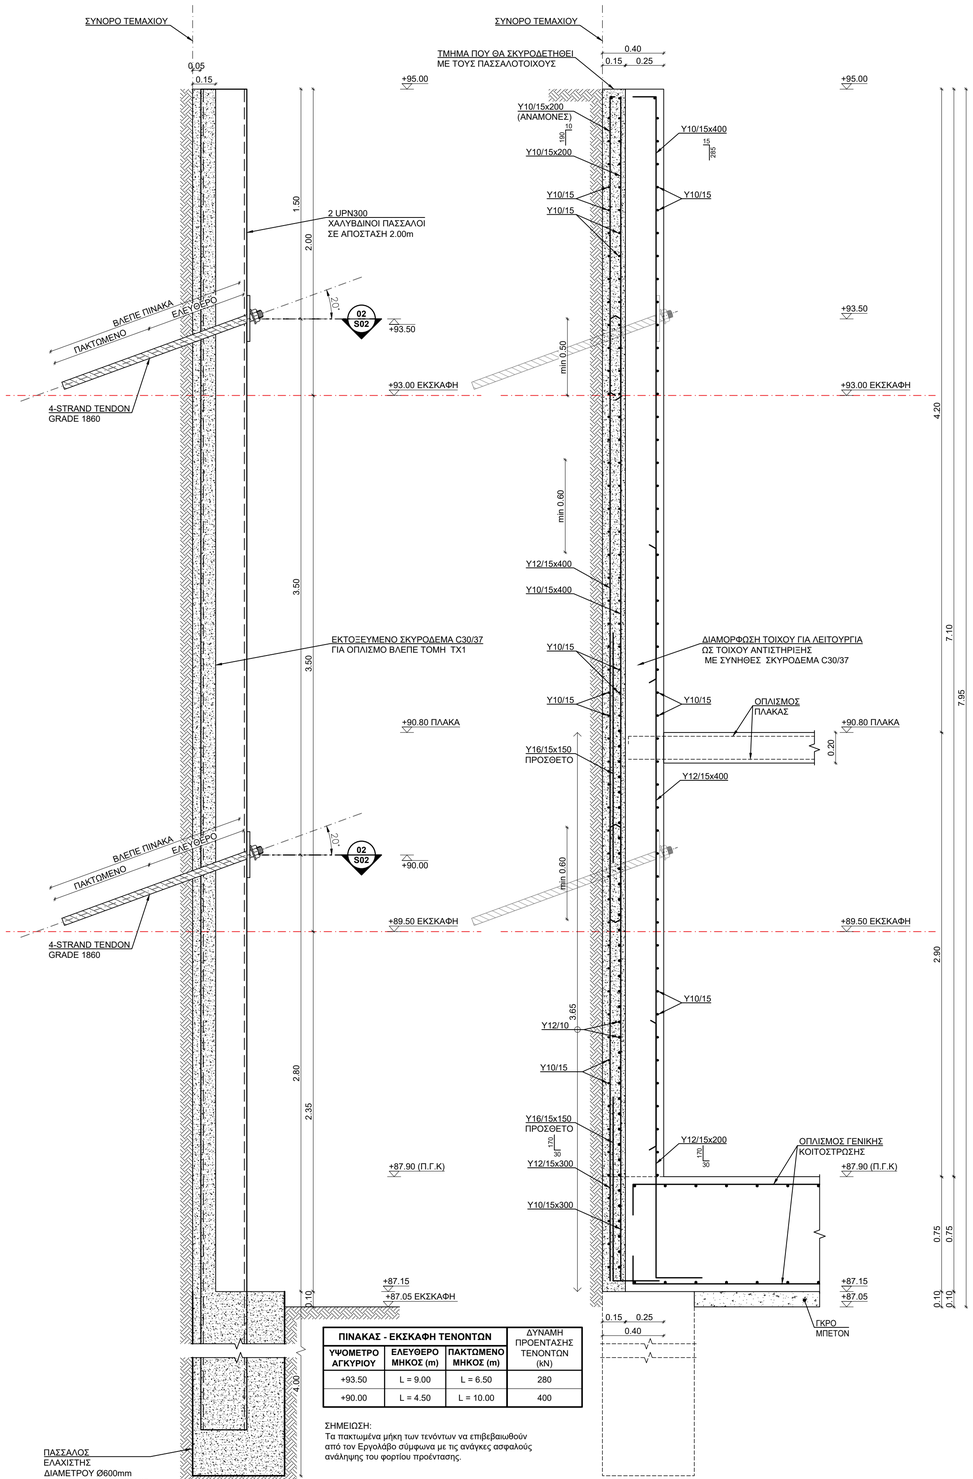


ΠΙΝΑΚΑΣ - ΕΚΣΚΑΦΗ ΤΕΝΟΝΤΩΝ			ΔΥΝΑΜΗ ΠΡΟΕΝΤΑΣΗΣ ΤΕΝΟΝΤΩΝ (kN)
ΥΨΟΜΕΤΡΟ ΑΓΚΥΡΙΟΥ	ΕΛΕΥΘΕΡΟ ΜΗΚΟΣ (m)	ΠΑΚΤΩΜΕΝΟ ΜΗΚΟΣ (m)	
+93.50	L = 9.00	L = 6.50	280
+90.00	L = 4.50	L = 10.00	400

ΣΗΜΕΙΩΣΗ:
Τα πακτωμένα μήκη των τενόντων να επιβεβαιωθούν από τον Εργολάβο σύμφωνα με τις ανάγκες ασφαλούς ανάληψης του φορτίου προέντασης.


ΤΟΜΗ 01 ΑΝΤΙΣΤΗΡΙΞΗ ΕΚΣΚΑΦΗΣ

ΚΛΙΜΑΚΑ 1:20

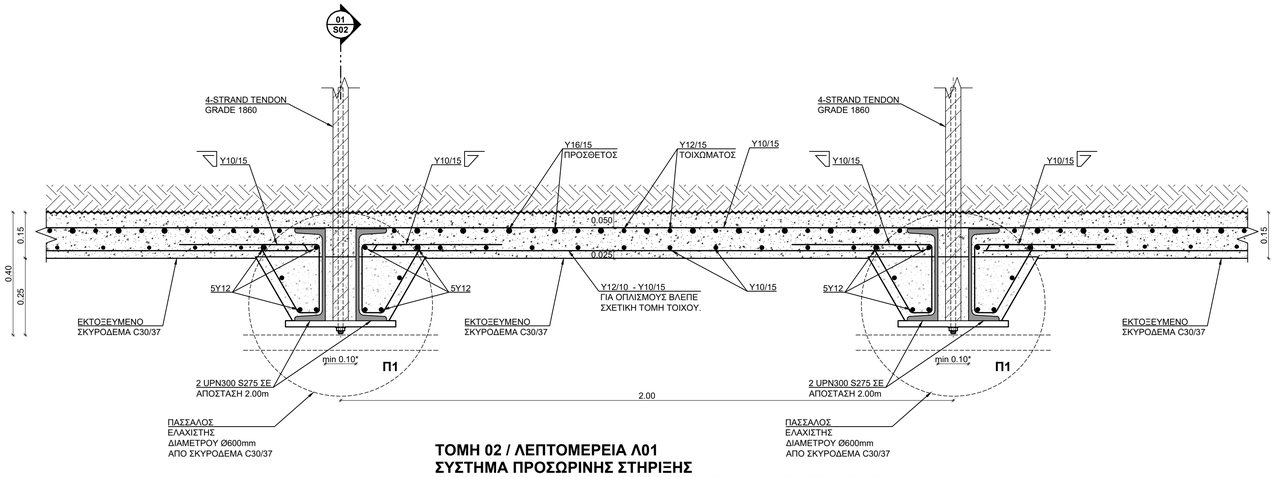


ΤΟΜΗ 02 / ΛΕΠΤΟΜΕΡΕΙΑ Λ01
ΣΥΣΤΗΜΑ ΠΡΟΣΩΡΙΝΗΣ ΣΤΗΡΙΞΗΣ ΕΚΣΚΑΜΜΕΝΟΥ ΕΔΑΦΟΥΣ ΜΕ ΧΑΛΥΒΔΙΝΟΥΣ ΠΑΣΣΑΛΟΥΣ

ΚΛΙΜΑΚΑ 1:10

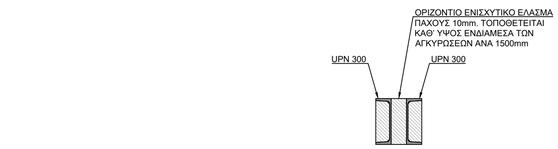

ΤΥΠΙΚΗ ΤΟΜΗ ΤΤ

ΚΛΙΜΑΚΑ 1:20

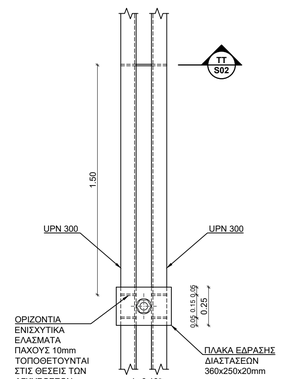

ΤΥΠΙΚΗ ΛΕΠΤΟΜΕΡΕΙΑ

ΚΛΙΜΑΚΑ 1:20

ΠΑΡΑΤΗΡΗΣΕΙΣ / NOTES

ΓΕΝΙΚΕΣ

1. ΠΟΙΟΤΗΤΑ ΣΥΝΗΘΙΣΜΕΝΟΥ ΚΑΙ ΕΚΤΟΞΕΥΟΜΕΝΟΥ ΣΚΥΡΟΔΕΜΑΤΟΣ C30/37 ΕΛΑΧΙΣΤΗΣ ΧΑΡΑΚΤΗΡΙΣΤΙΚΗΣ ΟΛΙΠΤΙΚΗΣ ΑΝΤΟΧΗΣ ΚΥΛΙΝΔΡΙΚΟΥ ΔΟΚΙΜΙΟΥ ΣΤΙΣ 28 ΗΜΕΡΕΣ f_{ck}=30N/mm².
2. ΠΟΙΟΤΗΤΑ ΣΚΥΡΟΔΕΜΑΤΟΣ ΕΞΟΜΑΛΥΝΣΗΣ - GROSS BETON C12/15 ΕΛΑΧΙΣΤΗΣ ΧΑΡΑΚΤΗΡΙΣΤΙΚΗΣ ΟΛΙΠΤΙΚΗΣ ΑΝΤΟΧΗΣ ΚΥΛΙΝΔΡΙΚΟΥ ΔΟΚΙΜΙΟΥ ΣΤΙΣ 28 ΗΜΕΡΕΣ f_{ck}=12N/mm².
3. Ο ΟΠΛΙΣΜΟΣ ΕΙΝΑΙ ΠΑΝΤΟΥ ΥΨΗΛΗΣ ΑΝΤΟΧΗΣ B500C ΕΛΑΧΙΣΤΗΣ ΧΑΡΑΚΤΗΡΙΣΤΙΚΗΣ ΑΝΤΟΧΗΣ - ΟΡΙΟΥ ΔΙΑΡΡΟΗΣ f_{yk}=500N/mm².
4. ΕΠΙΚΑΛΥΨΗ ΟΠΛΙΣΜΩΝ ΣΕ:
   - ΤΟΙΧΩΜΑΤΑ 30 mm
   - ΤΟΙΧΩΜΑΤΑ - ΠΛΕΥΡΑ ΣΕ ΕΠΑΦΗ ΜΕ ΕΔΑΦΟΣ 50 mm

   ΕΚΤΟΣ ΚΑΙ ΑΝ ΑΝΑΓΡΑΦΕΤΑΙ ΔΙΑΦΟΡΕΤΙΚΑ ΣΤΑ ΣΧΕΔΙΑ.
5. ΤΟ ΜΗΚΟΣ ΥΠΕΡΚΑΛΥΨΗΣ (LAP SPLICE) ΣΤΙΣ ΕΝΩΣΕΙΣ ΤΩΝ ΟΠΛΙΣΜΩΝ ΕΙΝΑΙ ΠΕΝΗΝΤΑ ΦΟΡΕΣ Η ΔΙΑΜΕΤΡΟΣ (ΔΙΑΤΟΜΗ) ΤΟΥ ΜΙΚΡΟΤΕΡΟΥ ΟΠΛΙΣΜΟΥ ΠΟΥ ΕΝΩΝΕΤΑΙ (50$x d_{bar}$).

ΔΙΑΤΟΜΗ ΣΙΔΗΡΟΥ	ΜΗΚΟΣ (cm)
Y12	60
Y16	80
Y20	100

ΔΙΑΤΟΜΗ ΣΙΔΗΡΟΥ	ΜΗΚΟΣ (cm)
Y25	125
Y28	140
Y32	160

6. ΓΙΑ ΤΗ ΜΟΡΦΗ ΕΜΦΑΝΙΣΗΣ ΤΗΣ ΤΕΛΙΚΗΣ ΕΠΙΦΑΝΕΙΑΣ ΤΟΥ ΣΚΥΡΟΔΕΜΑΤΟΣ (ΚΑΘΟΡΙΣΜΟΣ ΤΥΠΟΥ ΞΥΛΟΤΥΠΟΥ) ΣΕ ΠΛΑΚΕΣ, ΔΟΚΟΥΣ, ΥΠΟΣΤΥΛΩΜΑΤΑ ΚΑΙ ΤΟΙΧΩΜΑΤΑ ΒΛΕΠΕ ΑΡΧΙΤΕΚΤΟΝΙΚΑ ΣΧΕΔΙΑ ΚΑΙ ΟΔΗΓΙΕΣ.
7. ΟΙ ΔΙΑΣΤΑΣΕΙΣ ΚΑΙ ΤΑ ΥΨΟΜΕΤΡΑ ΠΟΥ ΑΝΑΓΡΑΦΟΝΤΑΙ ΣΤΑ ΣΤΑΤΙΚΑ ΣΧΕΔΙΑ ΝΑ ΕΛΕΓΧΟΝΤΑΙ ΜΕ ΑΥΤΑ ΤΩΝ ΑΡΧΙΤΕΚΤΟΝΙΚΩΝ ΣΧΕΔΙΩΝ.
8. ΝΑ ΧΡΗΣΙΜΟΠΟΙΗΘΕΙ ΠΡΟΣΜΕΙΚΤΟ ΥΠΕΡΡΛΑΣΤΙΚΟΠΟΙΗΤΗ (SUPERPLASTICIZER) ΤΡΙΤΗΣ ΓΕΝΕΑΣ, ΤΥΠΟΥ GLENIUM Η' ΑΛΛΟΥ ΠΑΡΟΜΟΙΟΥ ΥΛΙΚΟΥ, ΤΗΣ ΕΓΚΡΙΣΗΣ ΤΟΥ Ε.Μ. ΣΤΙΣ ΕΡΓΑΣΙΕΣ ΣΚΥΡΟΔΕΜΑΤΟΣ ΠΟΥ ΑΦΟΡΟΥΝ:
   - ΤΟΙΧΩΜΑΤΑ
11. ΓΙΑ ΟΛΕΣ ΤΙΣ ΕΡΓΑΣΙΕΣ ΠΟΥ ΑΦΟΡΟΥΝ ΤΑ ΠΕΡΙΜΕΤΡΙΚΑ ΦΕΡΟΝΤΑ ΣΤΟΙΧΕΙΑ ΤΟΥ ΥΠΟΓΕΙΟΥ - ΤΟΙΧΩΜΑΤΑ ΑΝΤΙΣΤΗΡΙΞΗΣ ΝΑ ΧΡΗΣΙΜΟΠΟΙΗΘΕΙ ΣΤΕΓΑΝΟΠΟΙΗΤΙΚΟ ΠΡΟΣΜΕΙΚΤΟ ΤΥΠΟΥ ΡΕΝΕΤΡΟΝ Η' ΑΛΛΟΥ ΠΑΡΟΜΟΙΟΥ ΥΛΙΚΟΥ ΤΗΣ ΕΓΚΡΙΣΗΣ ΤΟΥ Ε.Μ.

1. Οι τένοντες θα πρέπει να συμμορφώνονται προς τα πρότυπα DIN 1045 και pr EN1537 και pr EN 10138-3 και θα πρέπει να υποβληθούν σε δοκιμή με δύναμη προέντασης ίση με 1.3 φορές το φορτίο σχεδιασμού.

2. Δομικός χάλυβας κατηγορίας S275, εκτός αν αναγράφεται διαφορετικά

3. Συρματόσχοινα (strands) 15.2-mm, Grade 270 (metric 1860), εκτός αν αναγράφεται διαφορετικά

4. Οι δοκιμές των αγκυρίων πρέπει να εκτελούνται με βάση το πρότυπο EN ISO 22477-5 πριν την μεταφορά των δυνάμεων και την τελική λειτουργία τους.

5. Το καθαρό άνοιγμα μεταξύ των κατακόρυφων πασσάλων θα οριστεί από τον Εργολάβο βάσει των προδιαγραφών των τοποθετούμενων τενόντων και παρελκομένων.

D&K EPS LLC
Μελετητές & Σύμβουλοι Πολιτικοί Μηχανικοί
www.dkeps.com | A.M. ETEK: C00143

Γεώργιος Δημητριάδης
A.M. ETEK: A042573
Δίπλωμα Πολ. Μηχ. Ε.Μ.Π.
M.Sc S.U.N.Y at Buffalo
(Aseismic Base Isolation)
Διδυμότειχου 9, 3118 Λεμεσός
Τηλ. 25770978 Φαξ. 25770979
Email: dk_eps@spidernet.com.cy

Νίκος Καλαβάς
A.M. ETEK: A050668
Δίπλωμα Πολ. Μηχ. Ε.Μ.Π.
M.Sc U.C. at Berkeley
(Seismic Design & Engineering)
Αθηνών 111, 2035 Στρόβολος
Τηλ. 22495133 Φαξ. 22495123
Email: earth@spidernet.com.cy

ΤΙΤΛΟΣ ΕΡΓΟΥ / PROJECT TITLE
ΠΟΛΥΚΑΤΟΙΚΙΑ EMERALDA 5

ΤΙΤΛΟΣ ΣΧΕΔΙΟΥ / DRAWING TITLE
ΣΥΣΤΗΜΑ ΠΡΟΣΩΡΙΝΗΣ ΣΤΗΡΙΞΗΣ ΕΚΣΚΑΜΜΕΝΟΥ ΕΔΑΦΟΥΣ ΛΕΠΤΟΜΕΡΕΙΕΣ - ΤΟΜΕΣ

ΚΛΙΜΑΚΑ / SCALE	ΕΚΤΥΠΩΣΗ / PRINT
1:20 / 1:10	@ A1
ΦΑΣΗ ΣΧΕΔΙΑΣΜΟΥ / DESIGN PHASE	ΕΚΔΟΣΗ / VERSION
DETAILED DESIGN (DD)	01
ΗΜΕΡΟΜΗΝΙΑ / DATE	ΑΡ. ΣΧΕΔΙΟΥ / DRAWING NO
21/10/2026	S02
ΑΡ. ΜΕΛΕΤΗΣ / JOB NO	
S1480	

ΟΝΟΜΑ ΑΡΧΕΙΟΥ / FILE NAME
S1480_WALLS_DD_01.dwg
S1480_S02_DD_01.pdf