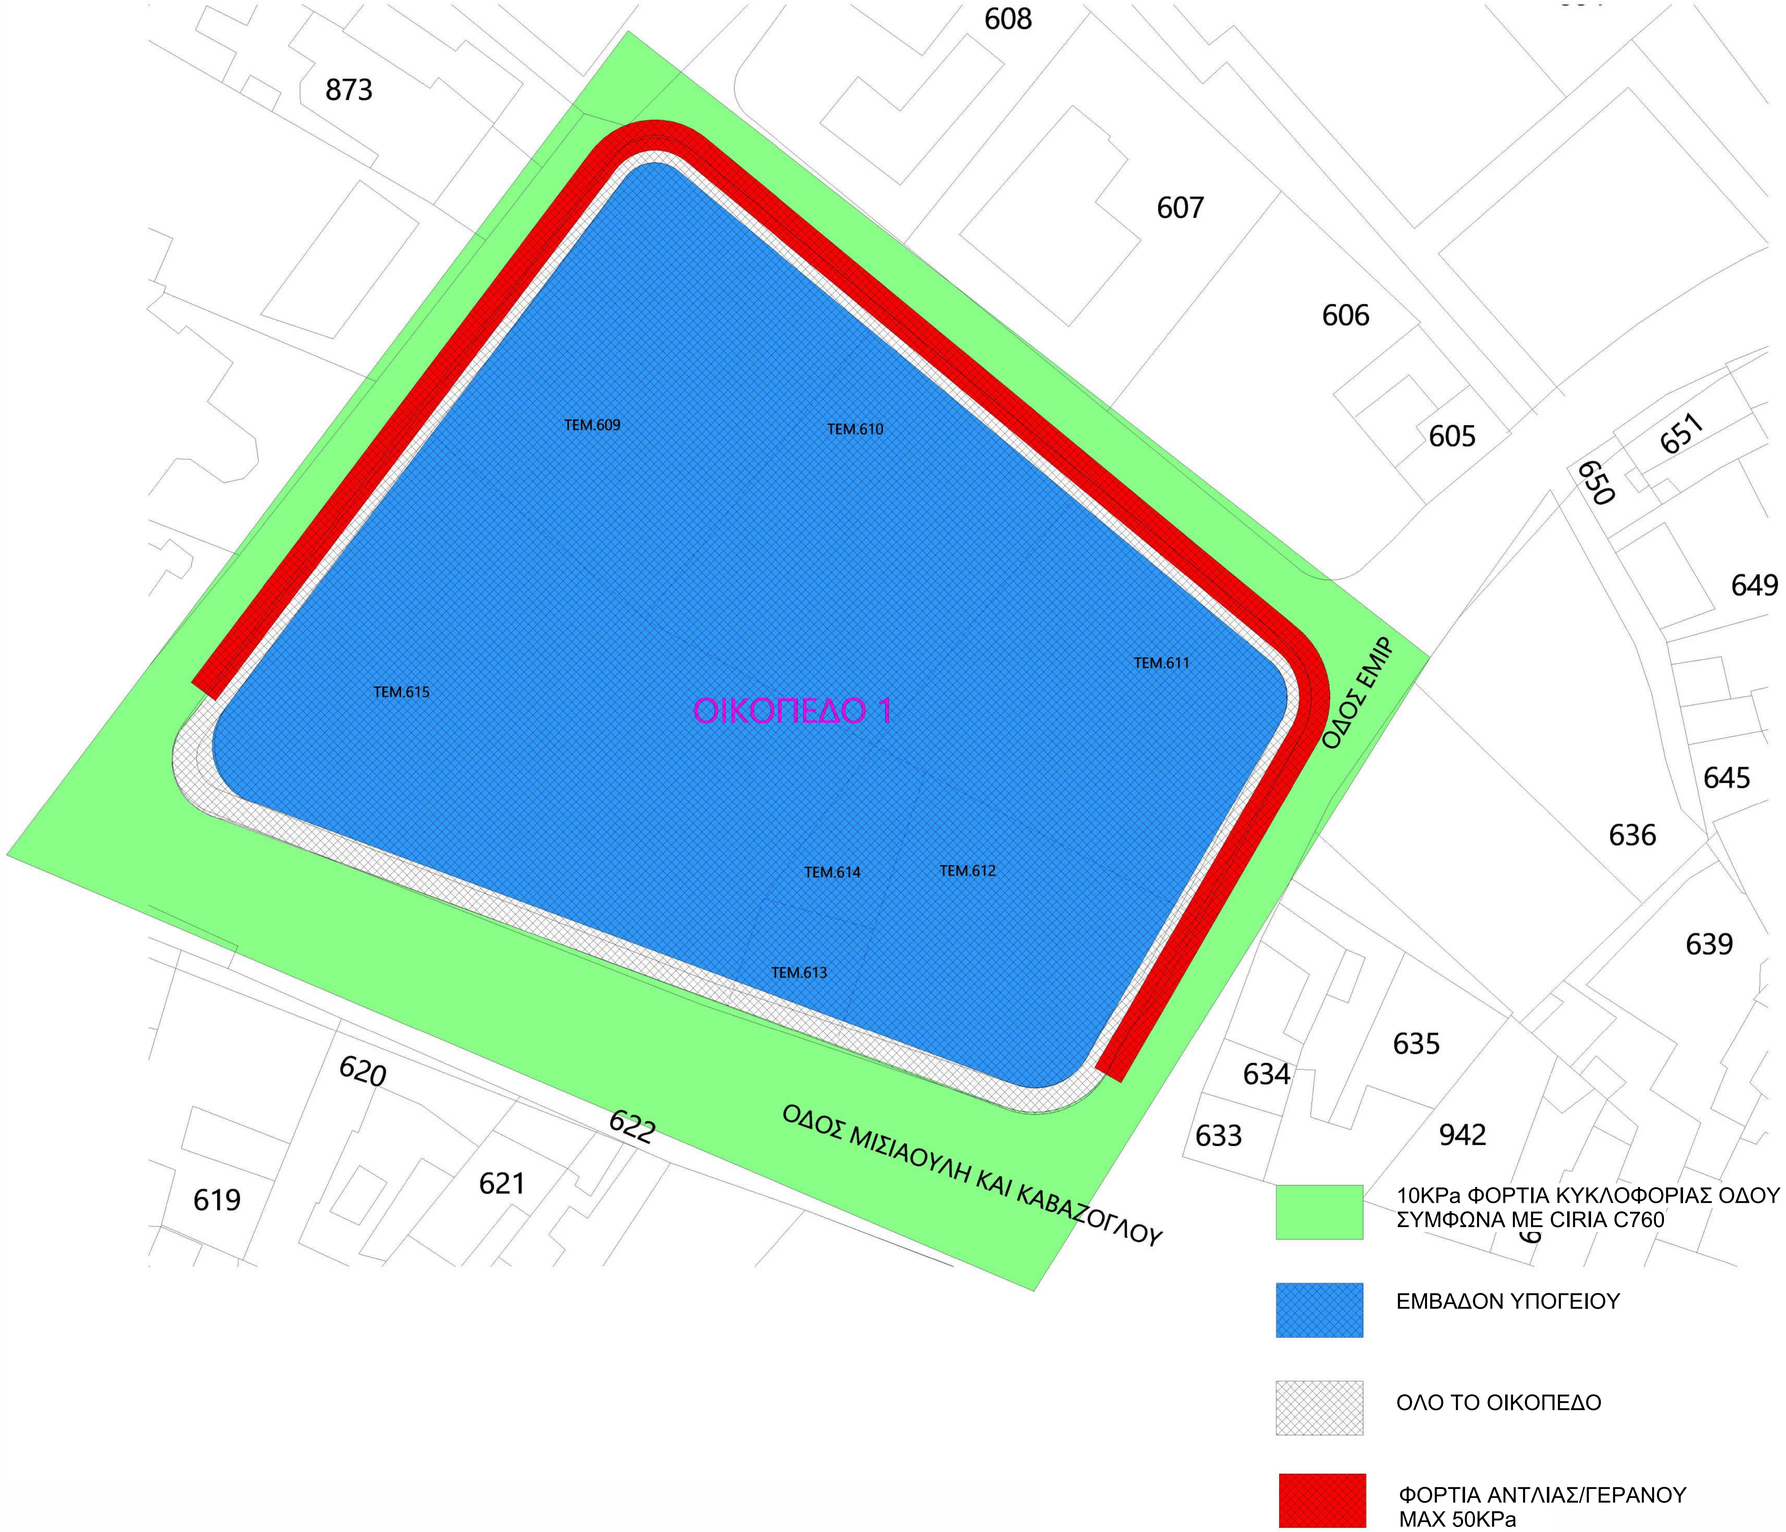


1 **ΚΑΤΟΨΗ ΟΙΚΟΠΕΔΟ - ΔΙΑΓΡΑΜΜΑ ΦΟΡΤΙΣΕΩΝ**
1 : 250

ΑΝΑΘ./ REV.	ΠΕΡΙΓΡΑΦΗ / DESCRIPTION	ΗΜΕΡ./ DATE
1	BUILDING PERMIT	07/10/2026

ΑΡΧΙΤΕΚΤΟΝΑΣ:

ARMEFTIS PARTNERS
29 ELENIS PALAIOLOGINAS STREET
3040 LIMASSOL, CYPRUS
PHONE: +35725828280
EMAIL: info@armeftis.com

ΠΟΛΙΤΙΚΟΣ ΜΗΧΑΝΙΚΟΣ

Evripidou Engineers

ANDREAS EVRIPIDOU CIVIL ENGINEERS L.L.C.
Αρ.Μητρώου ΕΤΕΚ: C00125

T: 22 820088
E: admin@evripidou-engineers.com
W: evripidou-engineers.com

ΥΠΟΓΡΑΦΩΝ ΜΗΧΑΝΙΚΟΣ

Ανδρέας Ευριπίδου
Διευθυντής της ANDREAS EVRIPIDOU CIVIL ENGINEERS L.L.C
Αρ. Μητρώου ΕΤΕΚ: A086614

ΣΤΑΔΙΟ ΜΕΛΕΤΗΣ: **BUILDING PERMIT**

ΕΡΓΟ: **The Hub**

ΑΡ.ΕΡΓΟΥ: **Μ.Π. 421**

ΗΜ.: **10/2026**

ΙΔΙΟΚΤΗΤΗΣ: **Cybarco Development Ltd**

ΤΙΤΛΟΣ ΣΧΕΔΙΟΥ:

ΠΡΟΣΩΡΙΝΗ ΑΝΤΙΣΤΗΡΙΞΗ ΕΚΣΚΑΦΗΣ ΔΙΑΓΡΑΜΜΑ ΦΟΡΤΙΣΕΩΝ

ΕΕ ΑΡ.ΕΡΓΟΥ: **Μ.Π. 421**


SCALE@A1: **As noted**

ΣΧΕΔΙΑΣΗ	ΕΛΕΓΧΟΣ:	ΕΓΚΡΙΣΗ
ΜΑ	**ΑΡ**	**ΑΕ**

ΑΡΙΘΜΟΣ ΣΧΕΔΙΟΥ: **CB01**

ΑΝΑΘΕΩΡΗΣΗ: **1**

© Evripidou Engineers LLC

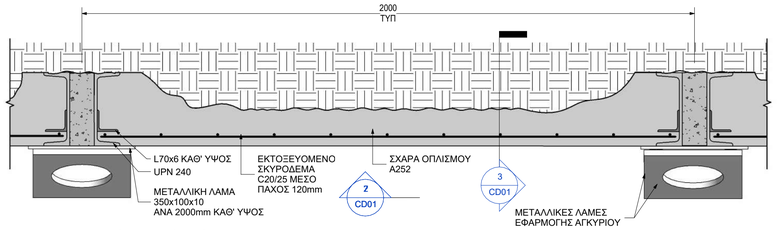


1 ΤΥΠΙΚΗ ΚΑΤΟΨΗ ΤΟΙΧΟΥ
1 : 10


ΥΛΙΚΑ:

1. ΑΓΚΥΡΙΑ
   - ΤΕΝΟΝΤΕΣ:
     ΚΑΤΗΓΟΡΙΑ S 1570/1770 ΜΙΚΡΗΣ ΧΑΛΑΡΩΣΗΣ
     E=195GPa
     d=15.3mm
   - ΕΝΕΜΑ ΠΑΚΤΩΣΗΣ:
     ΑΝΤΟΧΗ ΣΕ ΘΛΙΨΗ f_{gr}=35MPa
   - ΑΓΚΥΡΩΣΕΙΣ ΣΥΜΦΩΝΑ ΜΕ ΤΟ ΠΡΟΤΥΠΟ EN-150 22477

2. ΕΚΤΟΞΕΥΟΜΕΝΟ ΣΚΥΡΟΔΕΜΑ
   ΑΝΤΟΧΗ ΣΕ ΘΛΙΨΗ f_{gr}=20MPa
   ΟΠΛΙΣΜΟΣ A252 B500B


3. ΣΙΔΗΡΟΔΟΚΟΙ
   ΚΑΤΗΓΟΡΙΑ ΧΑΛΥΒΑ S275
   ΣΥΜΦΩΝΑ ΜΕ ΤΟ ΠΡΟΤΥΠΟ EN 10079
   ΤΟΠΟΘΕΤΗΣΗ ΣΙΔΗΡΟΔΟΚΟΥ ΣΥΜΦΩΝΑ ΜΕ ΤΟ ΠΡΟΤΥΠΟ EN 1536

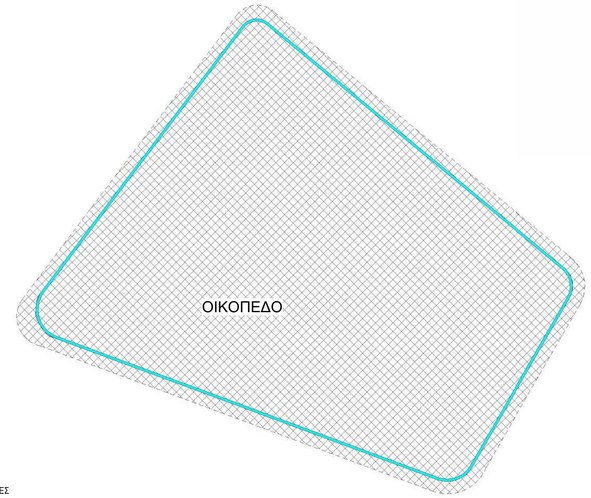

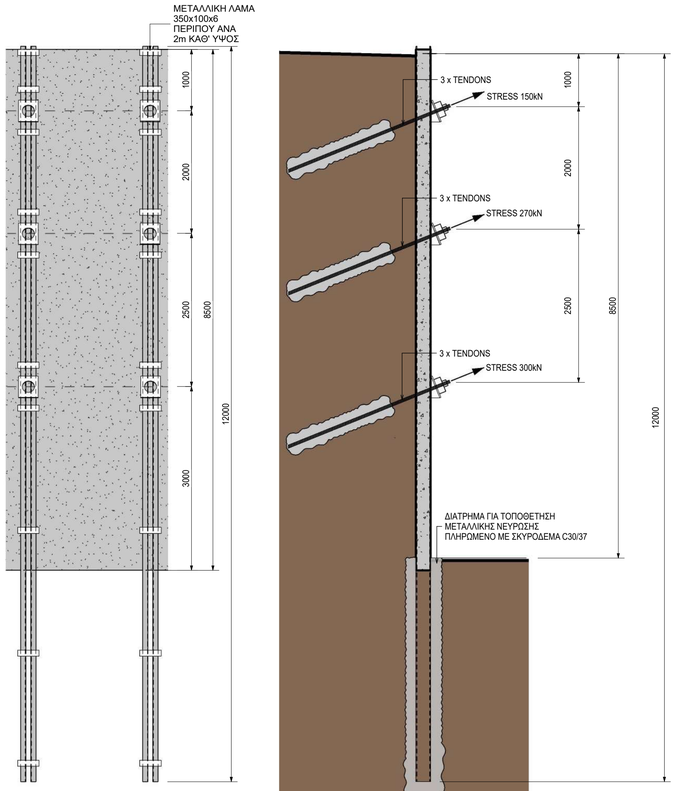


2 ΤΥΠΙΚΗ ΟΨΗ ΤΟΙΧΟΥ
1 : 50


3 ΤΥΠΙΚΗ ΤΟΜΗ ΤΟΙΧΟΥ
XK

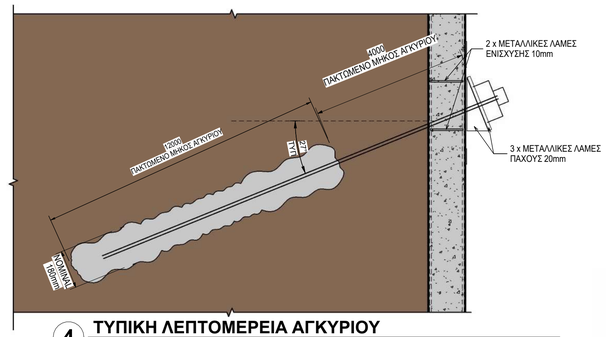


4 ΤΥΠΙΚΗ ΛΕΠΤΟΜΕΡΕΙΑ ΑΓΚΥΡΙΟΥ
XK

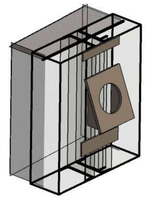

5 3D ΜΕΤΑΛΙΚΩΝ ΛΑΜΩΝ ΕΦΑΡΜΟΓΗΣ ΑΓΚΥΡΙΟΥ

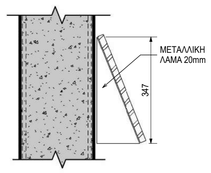


6 ΠΛΑΓΙΑ ΟΨΗ ΜΕΤΑΛΛΙΚΗΣ ΛΑΜΑΣ
1 : 10

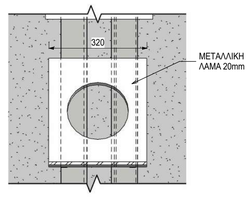

7 ΟΨΗ ΚΕΚΛΙΜΕΝΗΣ ΛΑΜΑΣ
1 : 10

ΣΗΜΕΙΩΣΕΙΣ:

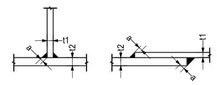

ΠΑΧΟΣ ΣΥΓΚΟΛΛΗΣΗΣ (a) ΓΙΑ ΦΛΑΝΤΖΑ ΠΑΧΟΥΣ<4mm: 3mm
ΠΑΧΟΣ ΣΥΓΚΟΛΛΗΣΗΣ (a) ΓΙΑ ΦΛΑΝΤΖΑ ΠΑΧΟΥΣ>4mm: 70%*(min(t1;t2))
ΕΚΤΟΣ ΑΝ ΑΝΑΓΡΑΦΕΤΑΙ ΔΙΑΦΟΡΕΤΙΚΑ

ΑΝΑΘ./ REV.	ΠΕΡΙΓΡΑΦΗ / DESCRIPTION	ΗΜΕΡ./ DATE
1	BUILDING PERMIT	07/10/2026

ΑΡΧΙΤΕΚΤΟΝΑΣ :

ARMEFTIS PARTNERS
29 ELENIS PALAIOLOGINAS STREET
3040 LIMASSOL, CYPRUS
PHONE: +35725828280
EMAIL: info@armeftis.com

ΠΟΛΙΤΙΚΟΣ ΜΗΧΑΝΙΚΟΣ

Evripidou Engineers

ANDREAS EVRIPIDOU CIVIL ENGINEERS L.L.C.
Αρ.Μητρώου ΕΤΕΚ: C00125

T: 22 820088
E: admin@evripidou-engineers.com
W: evripidou-engineers.com

ΥΠΟΓΡΑΦΩΝ ΜΗΧΑΝΙΚΟΣ

Ανδρέας Ευριπίδου
Διαχειρ/ντής της ANDREAS EVRIPIDOU CIVIL ENGINEERS L.L.C
Αρ. Μητρώου ΕΤΕΚ: A086614

ΣΤΑΔΙΟ ΜΕΛΕΤΗΣ: **BUILDING PERMIT**

ΕΡΓΟ :

The Hub

ΑΡ.ΕΡΓΟΥ: **Μ.Π. 421**

ΗΜ.: **10/2026**

ΙΔΙΟΚΤΗΤΗΣ:

Cybarco Development Ltd

ΤΙΤΛΟΣ ΣΧΕΔΙΟΥ:

ΠΡΟΣΩΡΙΝΟΣ ΤΟΙΧΟΣ ΑΝΤΙΣΤΗΡΙΞΗΣ ΤΥΠΟΥ 'ΒΕΡΟΛΙΝΟ'

ΕΕ ΑΡ.ΕΡΓΟΥ: **Μ.Π. 421**

SCALE@A1: **As noted**

ΣΧΕΔΙΑΣΗ	ΕΛΕΓΧΟΣ:	ΕΓΚΡΙΣΗ
ΜΑ	**ΑΡ**	**ΕΕ**

ΑΡΙΘΜΟΣ ΣΧΕΔΙΟΥ: **CD01**

ΑΝΑΘΕΩΡΗΣΗ : **1**

© Evripidou Engineers LLC