
**ΤΑ ΣΥΝΟΡΑ ΣΤΟ ΠΑΡΟΝ ΣΧΕΔΙΟ ΕΙΝΑΙ ΜΕ ΒΑΣΗ ΤΗΝ ΕΠΙΤΟΠΟΥ ΚΑΤΑΣΤΑΣΗ ΚΑΙ ΤΟ ΕΝ ΧΡΗΣΗ ΣΧΕΔΙΟ.

**ΤΑ ΤΕΛΙΚΑ ΣΥΝΟΡΑ ΘΑ ΔΟΘΟΥΝ ΟΤΑΝ ΟΛΟΚΛΗΡΩΘΕΙ Η ΕΠΙΣΗΜΗ ΕΞΩΤΕΡΙΚΗ ΟΡΙΟΘΕΤΗΣΗ.

**ΤΑ ΣΥΝΟΡΑ ΔΕΝ ΕΙΝΑΙ ΔΕΣΜΕΥΤΙΚΑ.

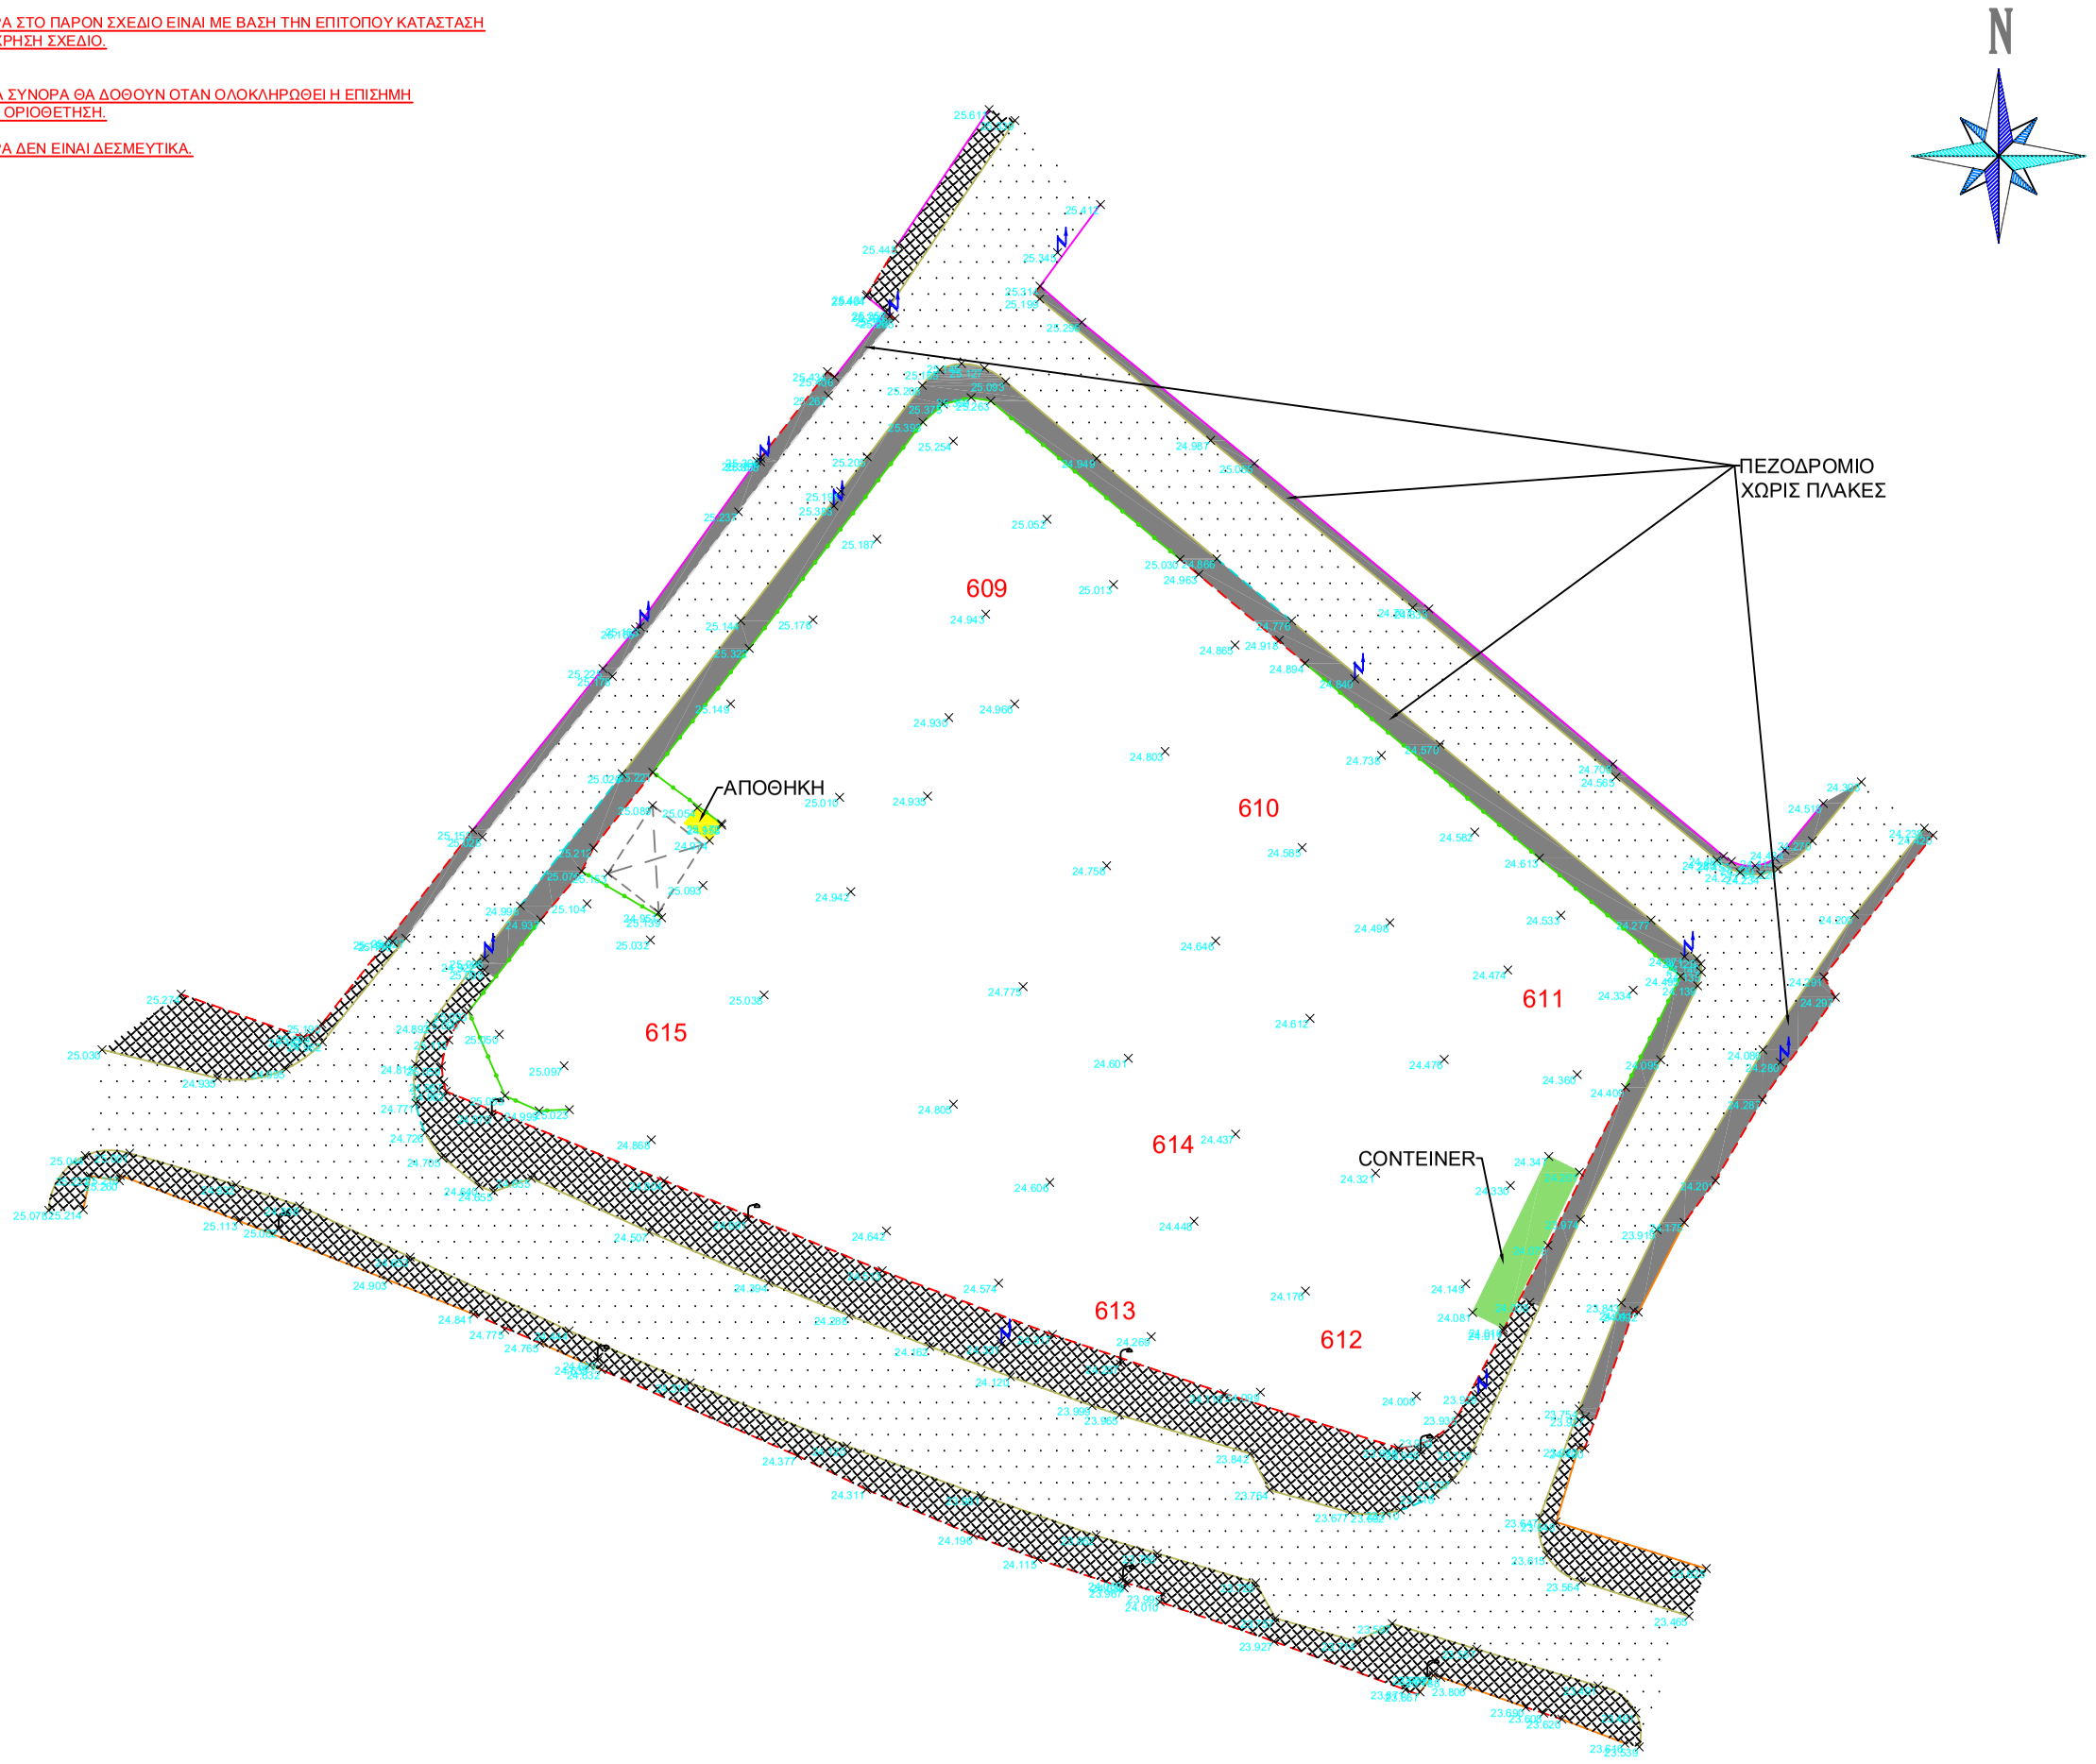

24.805 : ΥΨΟΜΕΤΡΑ ΕΔΑΦΟΥΣ

ΓΙΩΡΓΟΣ ΓΕΩΡΓΙΟΥ
Αγρονόμος Τοπογράφος Μηχανικός
Αρμόδιος Χωρομέτρης

Civil Engineering, Engineering Surveying Specialization BME

Τηλ.:99311990 Fax:25252303
e-mail: ggeorgiou@geoeasy.com.cy
info@geoeasy.com.cy

ΦΥΛΛΟ-ΣΧΕΔΙΟ	: 54/580403
ΑΡ. ΤΕΜΑΧΙΟΥ	: 609,610,611,612 613,614,615
ΤΜΗΜΑ	: 0
ΔΗΜΟΣ-ΕΝΟΡΙΑ	: ΛΕΜΕΣΟΣ,ΛΕΜΕΣΟΣ ΑΡΝΑΟΥΤΟΓΕΙΤΟΝΙΑ

GEOEASY L.L.C
LAND SURVEYORS-ENGINEERS

ΤΙΤΛΟΣ ΣΧΕΔΙΟΥ :

ΑΠΟΤΥΠΩΣΗ & ΥΨΟΜΕΤΡΗΣΗ ΥΦΙΣΤΑΜΕΝΗΣ ΚΑΤΑΣΤΑΣΗΣ ΤΕΜ. 609,610,611,612,613,614,615

ΚΛΙΜΑΚΑ ΕΚΤΥΠΩΣΗΣ	ΗΜΕΡΟΜΗΝΙΑ
1/500 A3	12/06/2026
ΚΛΙΜΑΚΑ ΣΧΕΔΙΑΣΗΣ 1/1	

ΑΡ. ΦΑΚΕΛΟΥ : 2026 - 080

ΥΠΟΓΡΑΦΗ / ΣΦΡΑΓΙΔΑ

Γιώργος Γεωργίου
Αγρονόμος Τοπογράφος Μηχανικός
Αρ. Μητρώου ΕΤΕΚ Α 28053

ΥΠΟΜΝΗΜΑ

- : ΛΙΝΙΑ
- : ΑΚΡΗ ΑΣΦΑΛΤΟΥ
- : ΑΚΡΗ ΠΕΖΟΔΡΟΜΙΟΥ
- : ΚΤΙΡΙΟ
- : ΠΕΡΙΤΟΙΧΙΣΜΑ
- : ΠΕΡΙΦΡΑΞΗ
- : CONTEINER
- : ΑΠΟΘΗΚΗ
- : ΕΙΣΟΔΟΣ ΟΙΚΟΠΕΔΟΥ
- : ΣΤΕΓΑΣΤΡΟ