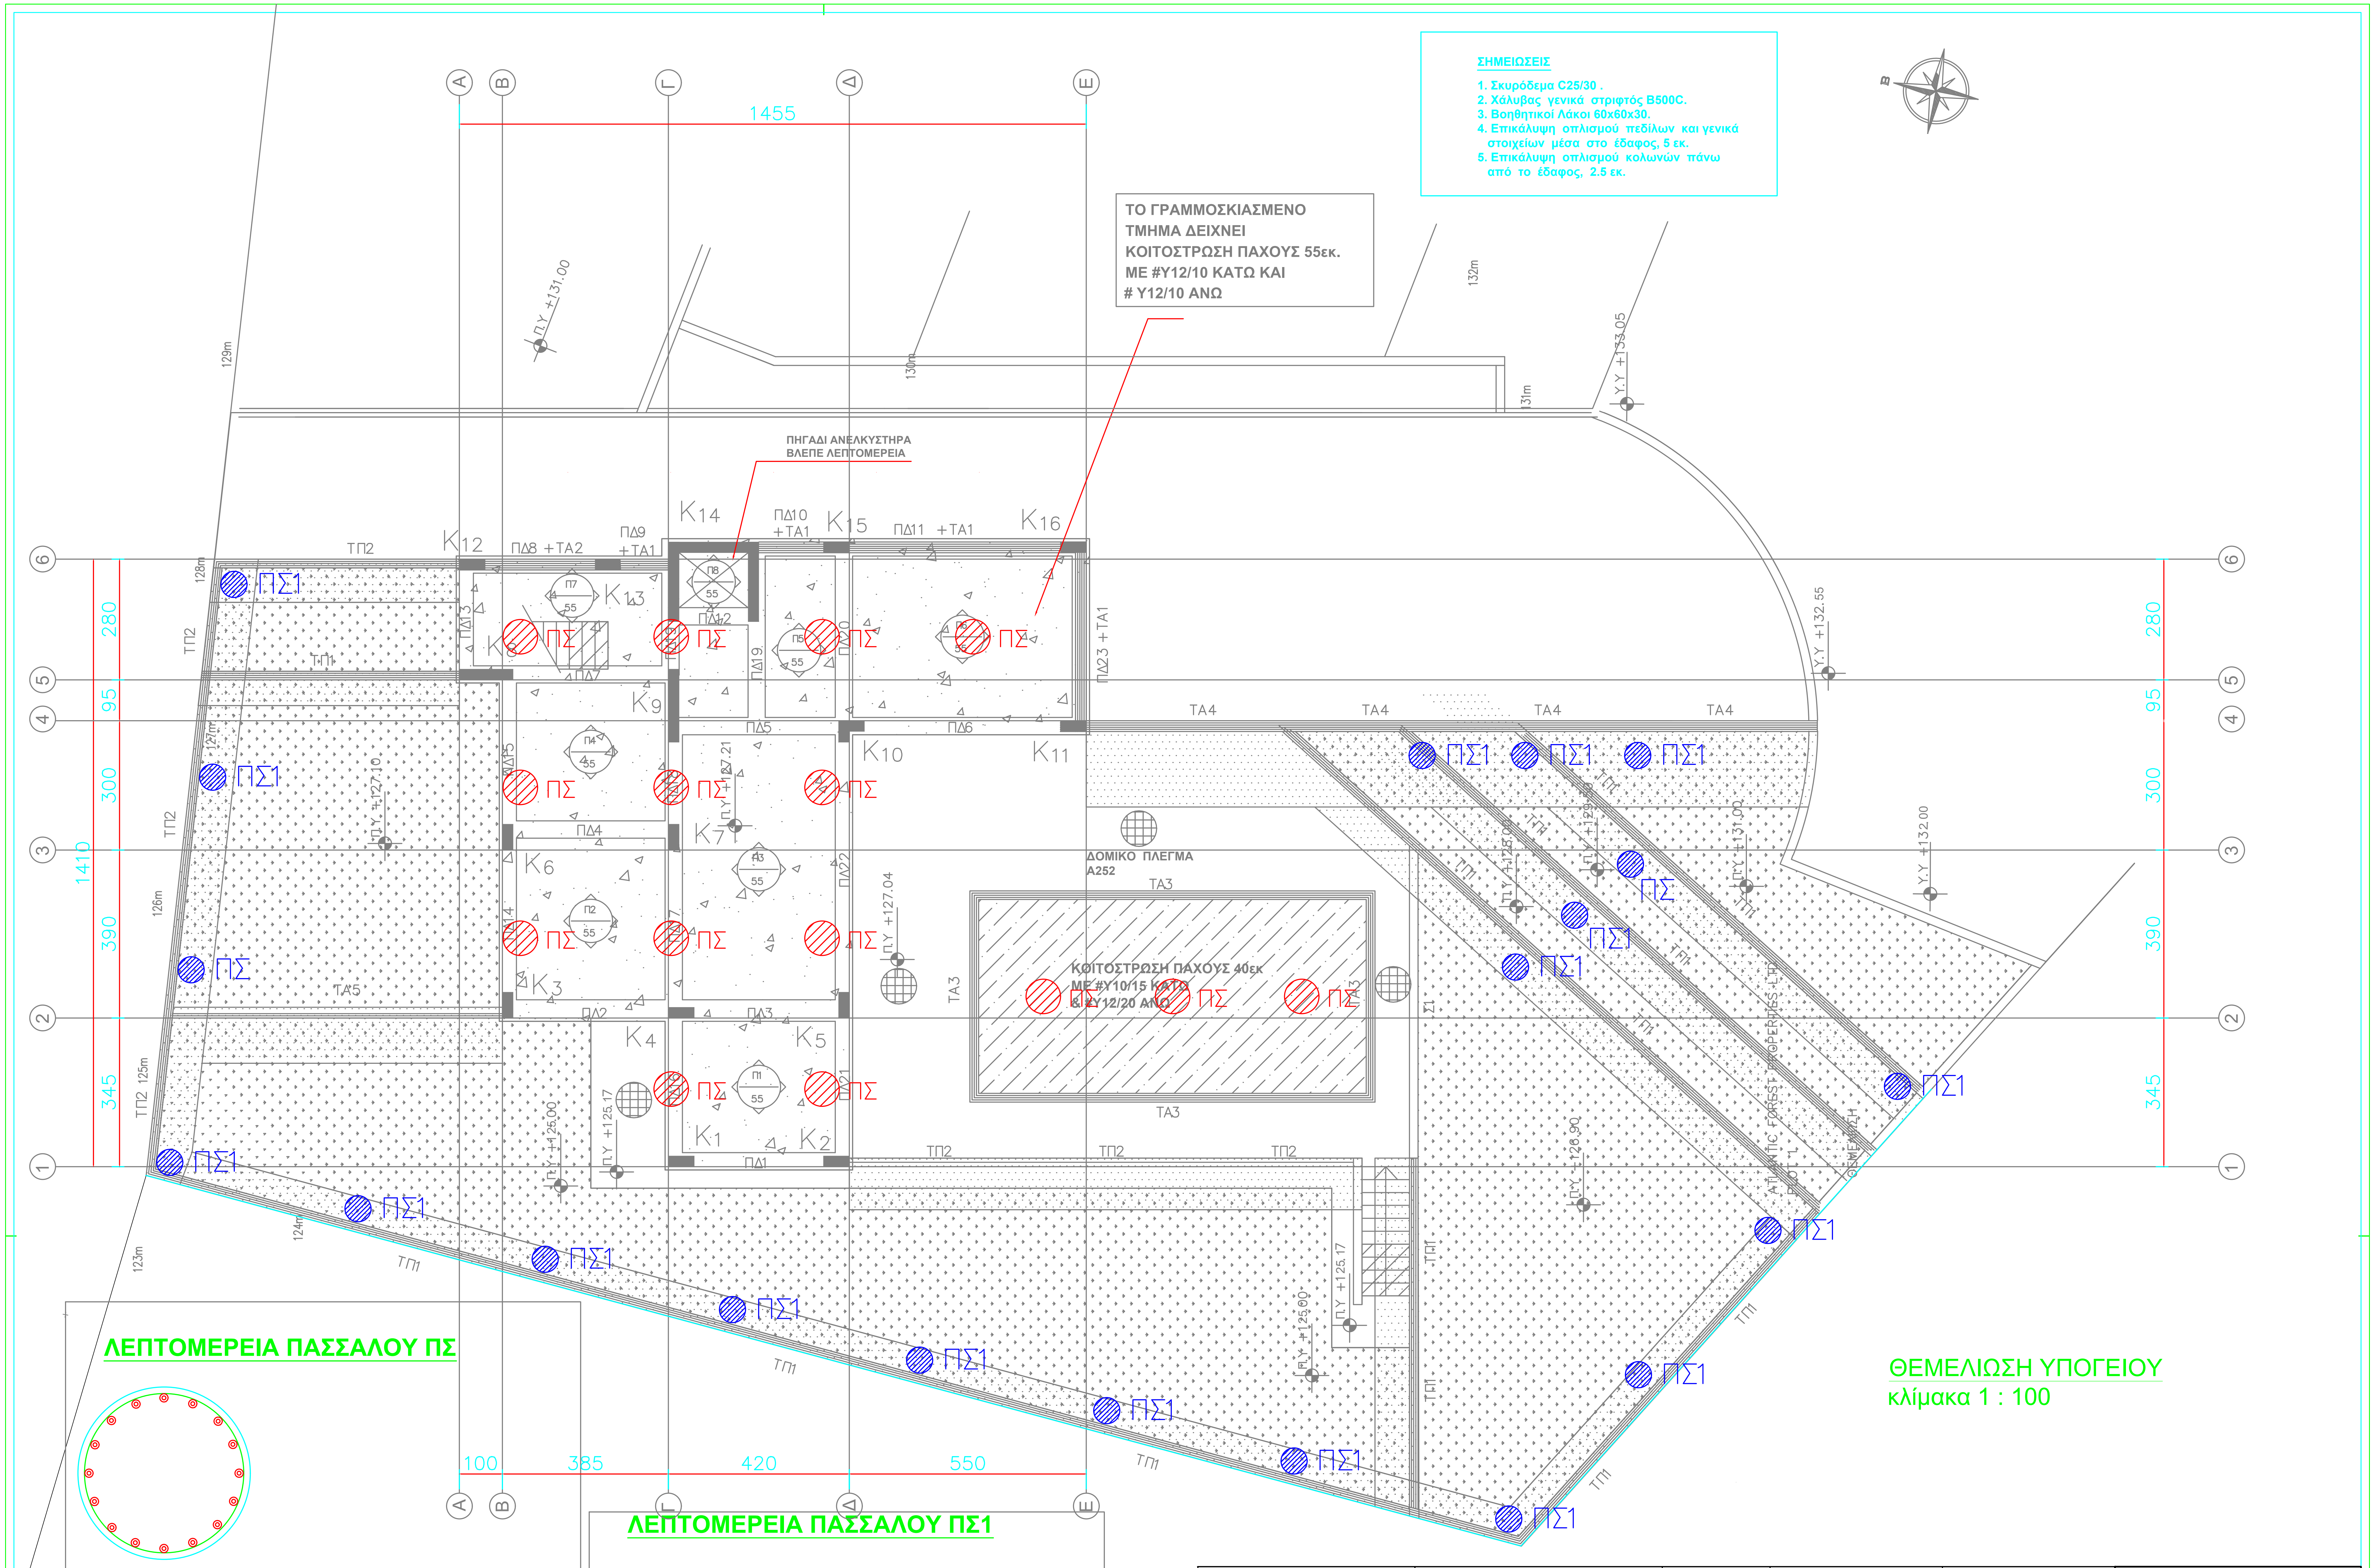

ΣΗΜΕΙΩΣΕΙΣ

1. Σκυρόδεμα C25/30 .
2. Χάλυβας γενικά στριφτός B500C.
3. Βοηθητικοί Λάκοι 60x60x30.
4. Επικάλυψη οπλισμού πεδίλων και γενικά στοιχείων μέσα στο έδαφος, 5 εκ.
5. Επικάλυψη οπλισμού κολωνών πάνω από το έδαφος, 2.5 εκ.

ΤΟ ΓΡΑΜΜΟΣΚΙΑΣΜΕΝΟ
ΤΜΗΜΑ ΔΕΙΧΝΕΙ
ΚΟΙΤΟΣΤΡΩΣΗ ΠΑΧΟΥΣ 55εκ.
ΜΕ #Υ12/10 ΚΑΤΩ ΚΑΙ
Υ12/10 ΑΝΩ

ΘΕΜΕΛΙΩΣΗ ΥΠΟΓΕΙΟΥ

κλίμακα 1 : 100

ΛΕΠΤΟΜΕΡΕΙΑ ΠΑΣΣΑΛΟΥ ΠΣ

ΠΑΣΣΑΛΟΣ ΠΣ ΔΙΑΜΕΤΡΟΥ 800mm
ΟΠΛΙΣΜΟΣ: 16Υ20
ΣΥΝΔΕΤΗΡΕΣ: ΣΠΕΙΡΟΕΙΔΕΙΣ Υ10/15.
ΒΑΘΟΣ 10m

ΛΕΠΤΟΜΕΡΕΙΑ ΠΑΣΣΑΛΟΥ ΠΣ1

ΚΑΘΕ 5m ΣΕ ΟΛΗ ΤΗ ΠΕΡΙΦΡΑΞΗ
ΠΑΣΣΑΛΟΣ ΠΣ1 ΔΙΑΜΕΤΡΟΥ 600mm
ΟΠΛΙΣΜΟΣ: 10Υ20
ΣΥΝΔΕΤΗΡΕΣ: ΣΠΕΙΡΟΕΙΔΕΙΣ Υ10/15.
ΒΑΘΟΣ 5m

ΠΑΡΑΤΗΡΙΣΕΙΣ - NOTES	ΟΙΚΟΔΟΜΗ - BUILDING	ΚΛΙΜΑΚΑ - SCALE	ΑΡ. ΣΧΕΔΙΟΥ - PROJECT No	ΑΡΧΙΤΕΚΤΟΝΑΣ _ ARCHITECT ΣΧΕΔΙΑΣΤΗΣ/ΡΙΑ DRAWN	ΠΑΝΙΚΟΣ Μ. ΧΑΡΙΛΑΟΥ ARCHITECT ENGINEER CONSULTANT
	ATLANTIC FOREST	A2/1:100			
	ΟΝΟΜΑ ΦΥΛΛΟΥ - SHEET TITLE	ΗΜΕΡ. - DATE	ΑΡ. ΦΥΛΛΟΥ - SHEET No	ΕΛΕΓΧΟΣ - CHECK	CORNER OF MAKARIOS AVE & APOSTOLOS BARNABAS STR. No2 P.O.Box 1764, Tel. 25 565350 LIMASSOL Fax: 25 564679–Car Tel. 99 636001
	PLOT 1 – ΠΑΣΣΑΛΟΙ ΣΕ ΚΑΤΟΨΗ	10/2026	00Σ		

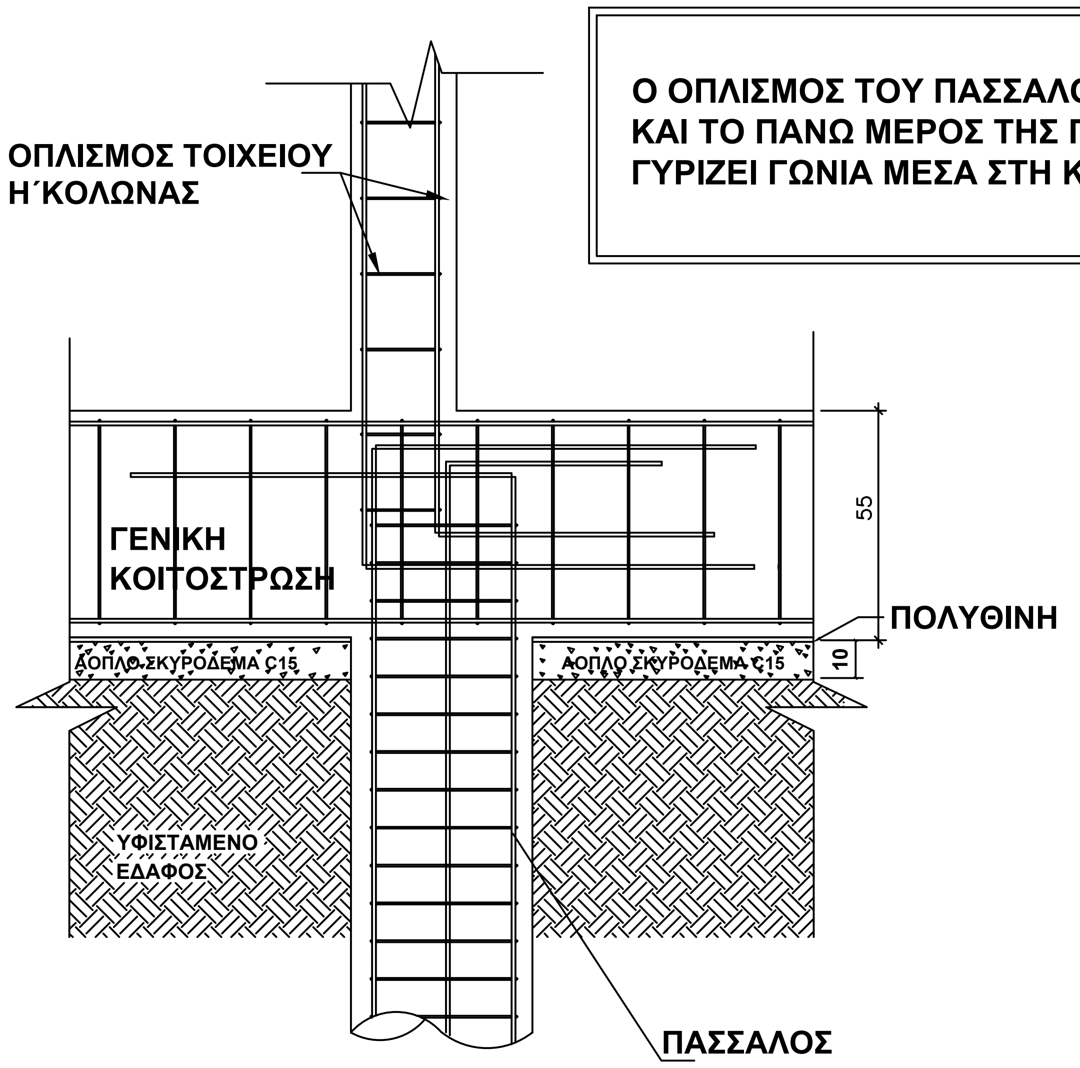

Ο ΟΠΛΙΣΜΟΣ ΤΟΥ ΠΑΣΣΑΛΟΥ ΝΑ ΣΥΝΕΧΙΖΕΙ ΜΕΧΡΙ ΚΑΙ ΤΟ ΠΑΝΩ ΜΕΡΟΣ ΤΗΣ ΠΕΔΙΛΟΚΟΥ ΚΑΙ ΝΑ ΓΥΡΙΖΕΙ ΓΩΝΙΑ ΜΕΣΑ ΣΤΗ ΚΟΙΤΟΣΤΡΩΣΗ.

ΛΕΠΤΟΜΕΡΕΙΑ ΠΑΣΣΑΛΟΥ
ΚΑΤΩ ΑΠΟ ΚΟΙΤΟΣΤΡΩΣΗ

ΚΛ. 1:20

ΛΕΠΤΟΜΕΡΕΙΑ ΠΑΣΣΑΛΟΥ ΠΣ

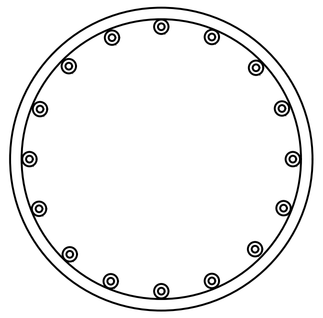

ΠΑΣΣΑΛΟΣ ΠΣ ΔΙΑΜΕΤΡΟΥ 800mm
ΟΠΛΙΣΜΟΣ: 16Υ20
ΣΥΝΔΕΤΗΡΕΣ: ΣΠΕΙΡΟΕΙΔΕΙΣ Υ10/15.
ΒΑΘΟΣ 10m

ΒΑΘΟΣ ΠΑΣΣΑΛΟΥ ΑΝΑΛΟΓΩΣ ΣΗΜΕΙΟΥ.
ΒΛΕΠΕ ΚΑΤΟΨΗ

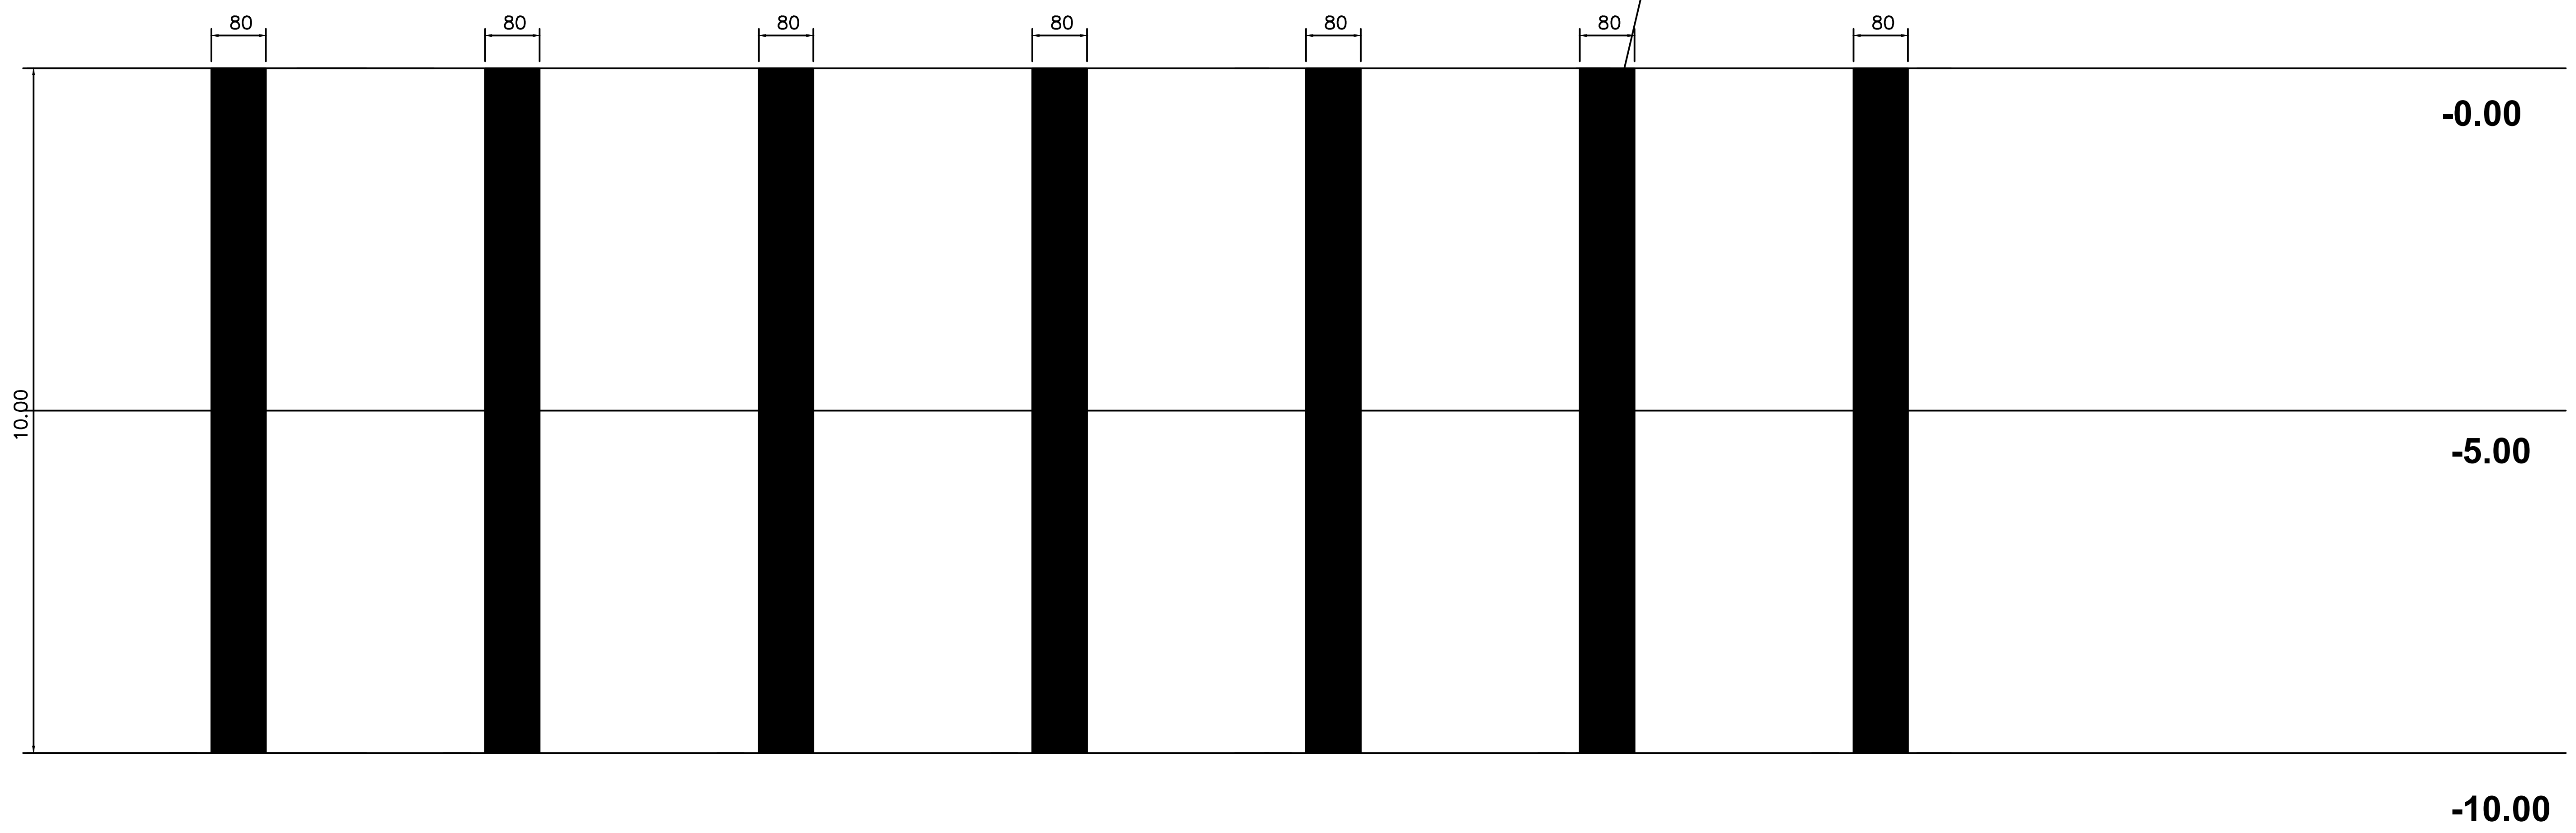

ΠΑΡΑΤΗΡΙΣΕΙΣ - NOTES	ΟΙΚΟΔΟΜΗ - BUILDING	ΚΛΙΜΑΚΑ - SCALE	ΑΡ. ΣΧΕΔΙΟΥ - PROJECT No	ΑΡΧΙΤΕΚΤΟΝΑΣ _ ARCHITECT ΣΧΕΔΙΑΣΤΗΣ/ΡΙΑ DRAWN	ΠΑΝΙΚΟΣ Μ. ΧΑΡΙΛΑΟΥ ARCHITECT ENGINEER CONSULTANT CORNER OF MAKARIOS AVE & APOSTOLOS BARNABAS STR. No2 P.O.Box 1764, Tel. 25 565350 LIMASSOL Fax: 25 564679—Car Tel. 99 636001
	ATLANTIC FOREST	A2/1:100			
	ΟΝΟΜΑ ΦΥΛΛΟΥ - SHEET TITLE	ΗΜΕΡ. - DATE	ΑΡ. ΦΥΛΛΟΥ - SHEET No	ΕΛΕΓΧΟΣ - CHECK	
	PLOT 1 – ΛΕΠΤΟΜΕΡΕΙΑ ΠΑΣΣΑΛΟΥ	10/2026	001Σ		